


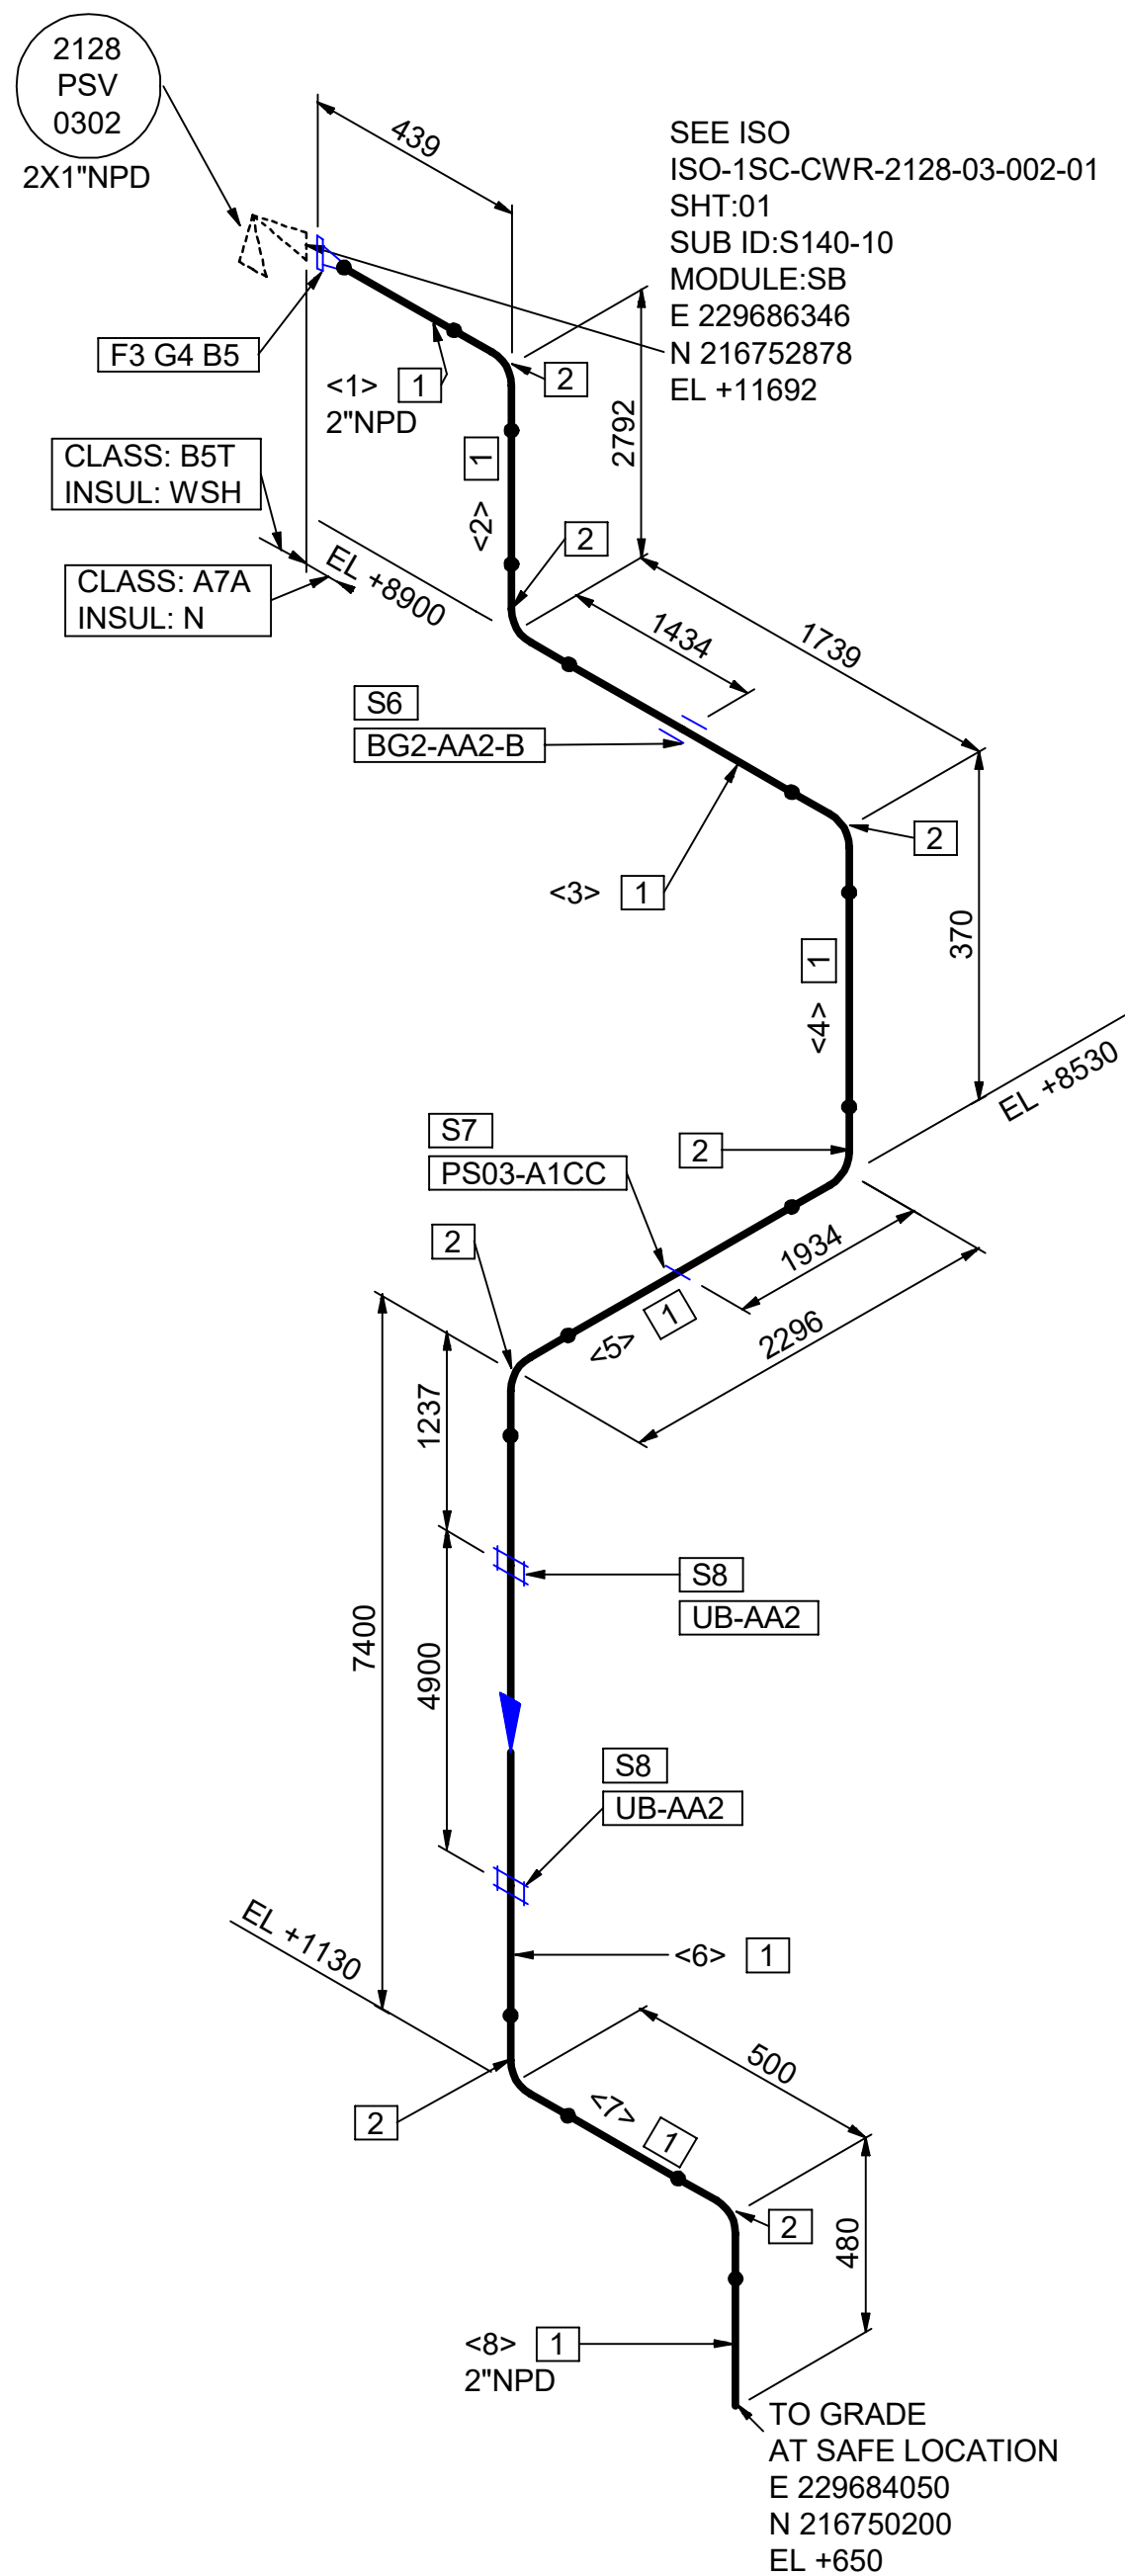

PACKAGE-1	HPP ELEVATION : 0.0 M (40.281M MSL, NGVD)
PACKAGE-2	HPP ELEVATION : 0.0 M (4.581M MSL, NGVD)
PACKAGE-3	HPP ELEVATION : 0.0 M (37.281M MSL, NGVD)
ODC,AREA-4	HPP ELEVATION : 29.0 M (32.781M MSL, NGVD)
RUC,AREA-1	ELEVATION : 3.781 M MSL, UL
RUC,AREA-2	ELEVATION : 16.281 M MSL, UL
EXIST. PLANT	ELEVATION : 3.781 M ~ 21.781 M MSL, UL

[illegible]

EXTRACTION DATE : 2024-10-07 19:57:05

SHOP MATERIALS

PT NO	MATERIALS DESCRIPTION	SIZE (IN)	MATERIAL CODE	QTY	MAT'L CLASS	INSUL TYPE
1	PIPE, CS API-5L-B-PSL1 ERW BE B36.10M S-STD	2	M289564823	14.9 M	A7A	N
2	90 DEG ELL LR, CS A234-WPB SMLS BE B16.9 S-STD	2	M197473210	7	A7A	N
3	WN FLG, CS A105 CL150 RF B16.5 S-STD Normalized	2	M238993878	1	A7A	N

FIELD MATERIALS

PT NO	MATERIALS DESCRIPTION	SIZE (IN)	MATERIAL CODE	QTY	MAT'L CLASS	INSUL TYPE
4	GSKT N-METAL F-RING, BUNA S CL150 RF B16.21 1.5MM THK	2	M290920165	1	A7A	N
5	STUD B W/H HEX N, AS A193 GR B7 / A194 GR 2H B18.31.2/B18.2.2 - 85 mm Length	5/8	M214072755	4	A7A	N

PIPE SUPPORTS

6	PIPING SUPPORT	2	BG2-AA2-B	1
7	PIPING SUPPORT	2	PS03-A1CC	1
8	PIPING SUPPORT	2	UB-AA2	2

CUT PIPE LENGTH


PIECE NO	LENGTH (MM)	NPD (IN)	REMARKS	PIECE NO	LENGTH (MM)	NPD (IN)	REMARKS
<1>	299	2		<2>	2640	2	
<3>	1587	2		<4>	218	2	
<5>	2144	2		<6>	7248	2	
<7>	348	2		<8>	404	2	

SHAHEEN PROJECT



HDL CONSORTIUM

PLANT	AREA	UNIT	P&ID NO.	SHAHEEN-2128-PR-PID-0003			
SSHN	SCC	U-212800		ISO DWG. NO.	ISO-1SC-ATM-2128-03-001-01	SHEET. NO	REV. NO
CWA	SUB ID	MODULE	01			0	
S140	S140-10	SB					

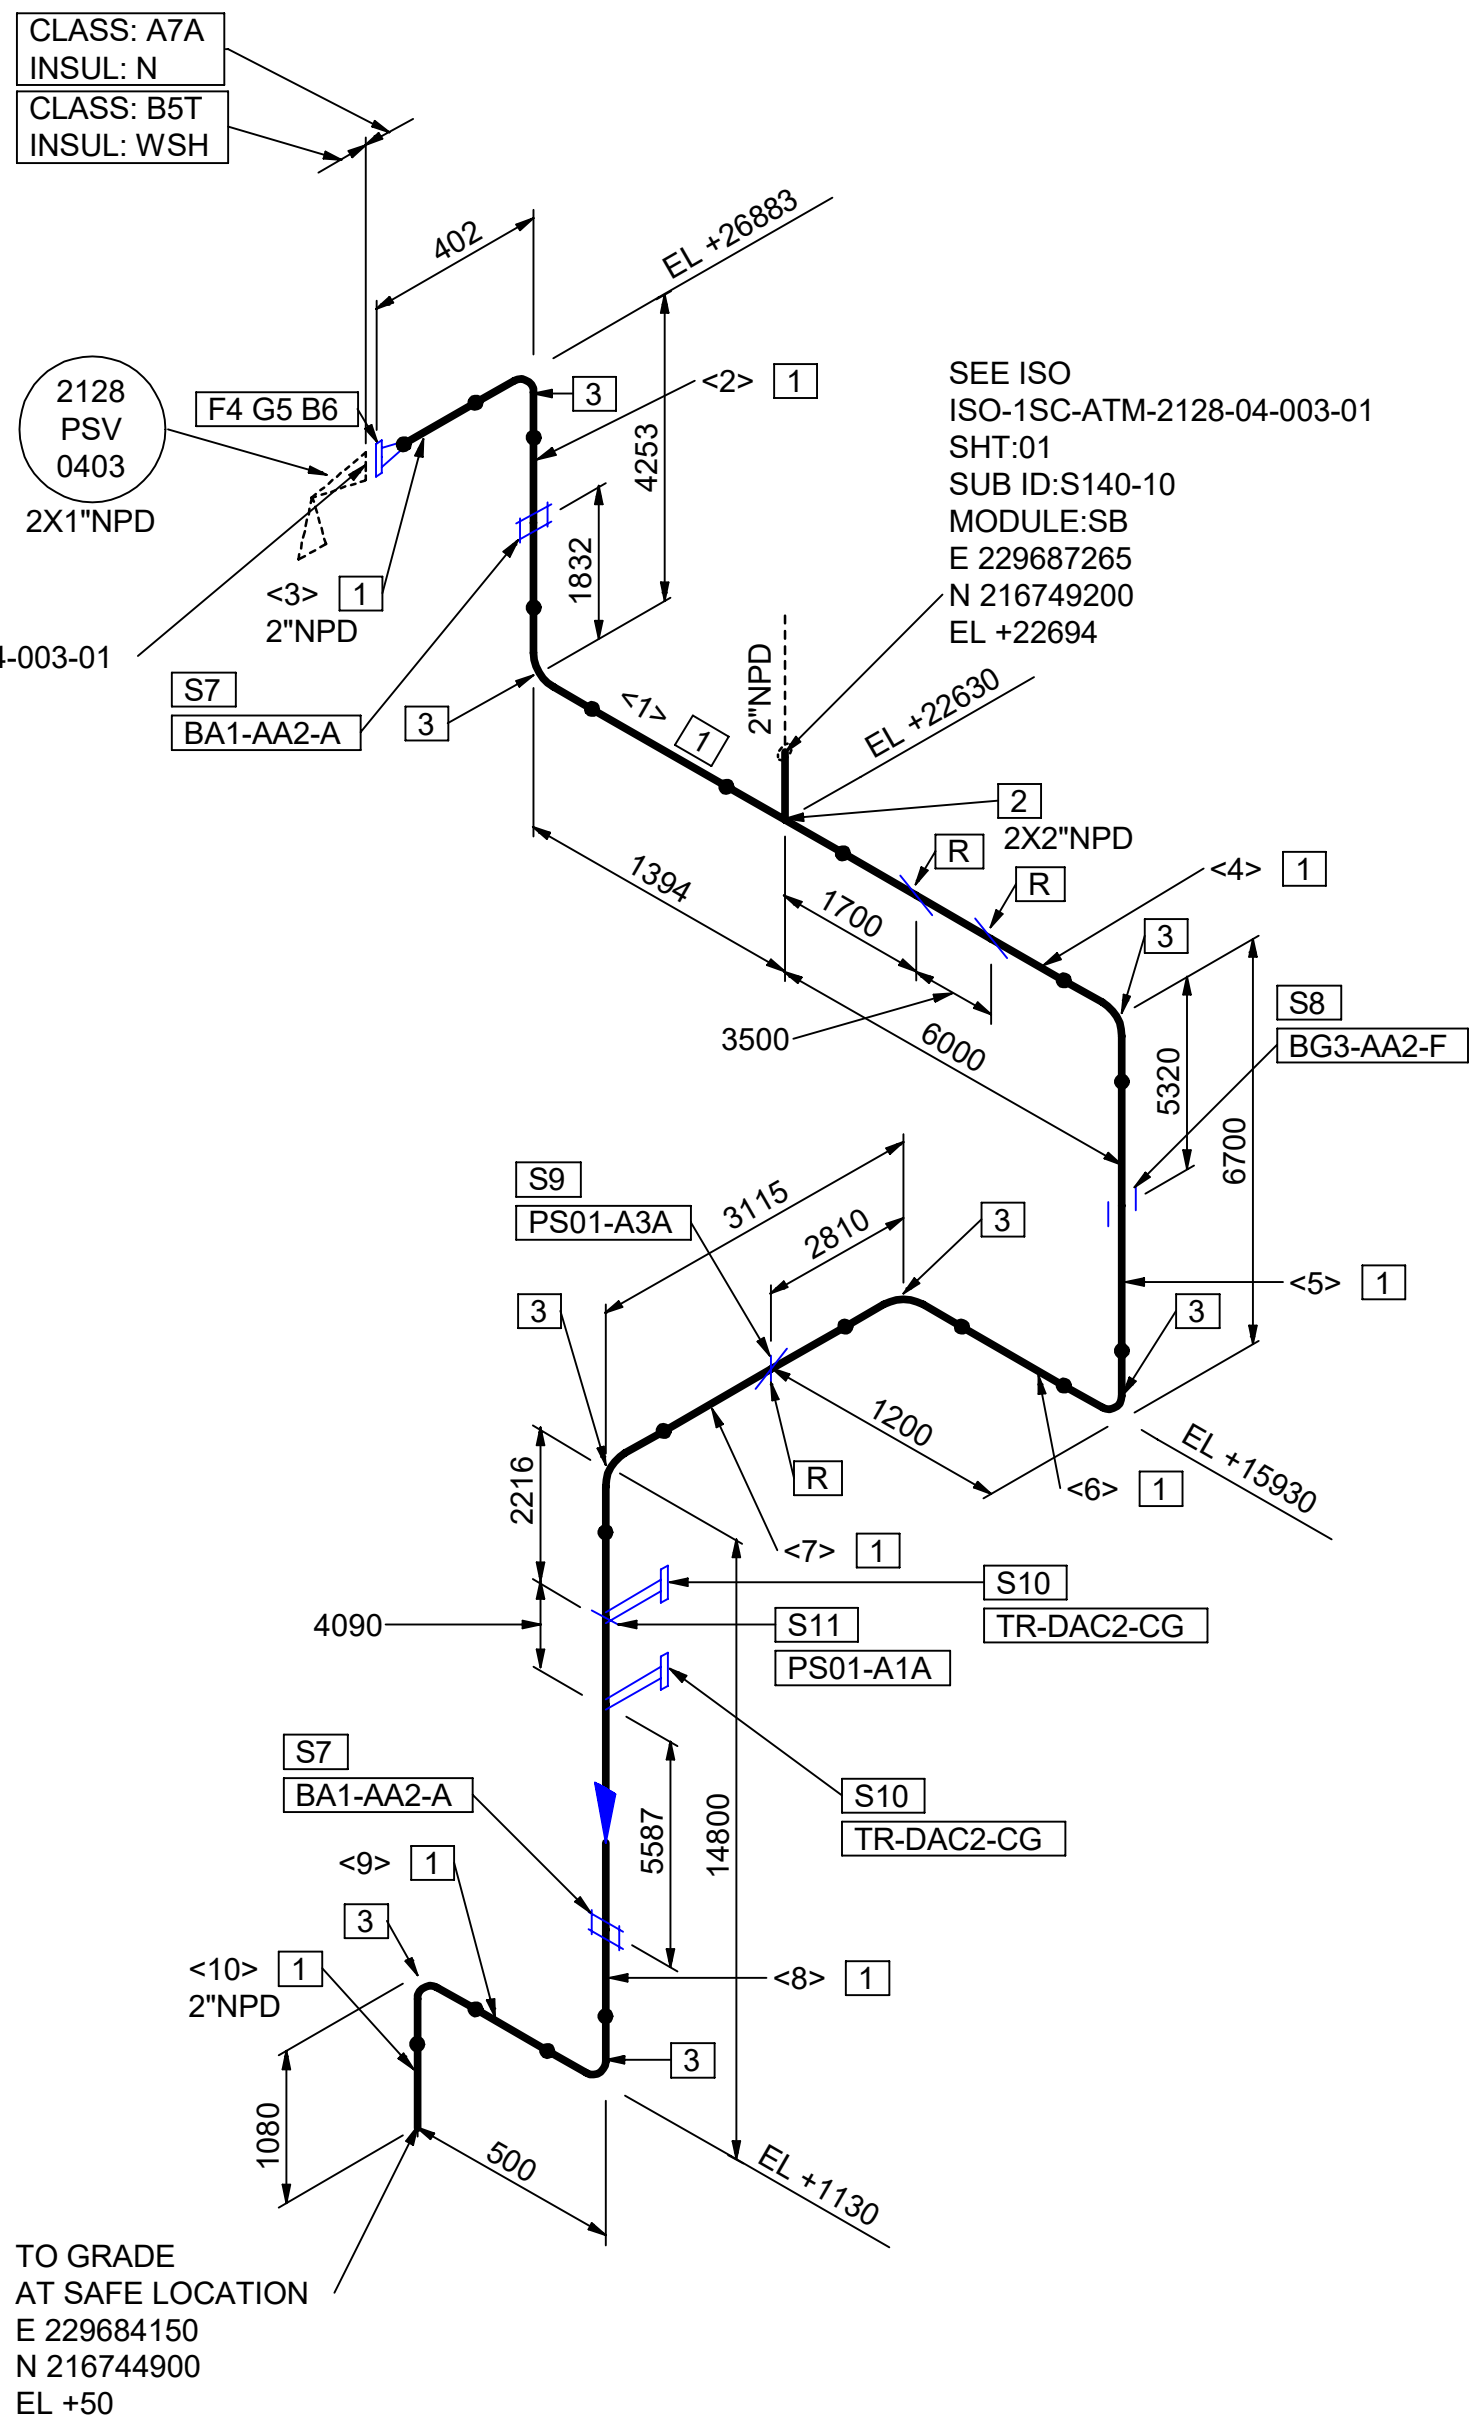

PACKAGE-1	HPP ELEVATION : 0.0 M (40.281M MSL, NGVD)
PACKAGE-2	HPP ELEVATION : 0.0 M (45.81M MSL, NGVD)
PACKAGE-3	HPP ELEVATION : 0.0 M (37.281M MSL, NGVD)
ODC,AREA-4	HPP ELEVATION : 29.0 M (32.781M MSL, NGVD)
RUC,AREA-1	ELEVATION : 3.781 M MSL, UL
RUC,AREA-2	ELEVATION : 16.281 M MSL, UL
EXIST. PLANT	ELEVATION : 3.781 M ~ 21.781 M MSL, UL

TO GRADE
AT SAFE LOCATION
E 229684150
N 216744900
EL +50

CLEANING CLASS : N	SERVICE PHASE : LIQUID	LOCAL REGULATION :	- KOSHA Guide D-10 : N
INSULATION MATERIAL :	SPECIAL REQUIREMENT : -		- CHEMICAL SUBSTANCES CONTROL ACT : N - HIGH PRESSURE GAS SAFETY CONTROL ACT : N

EXTRACTION DATE : 2024-10-07 20:02:05